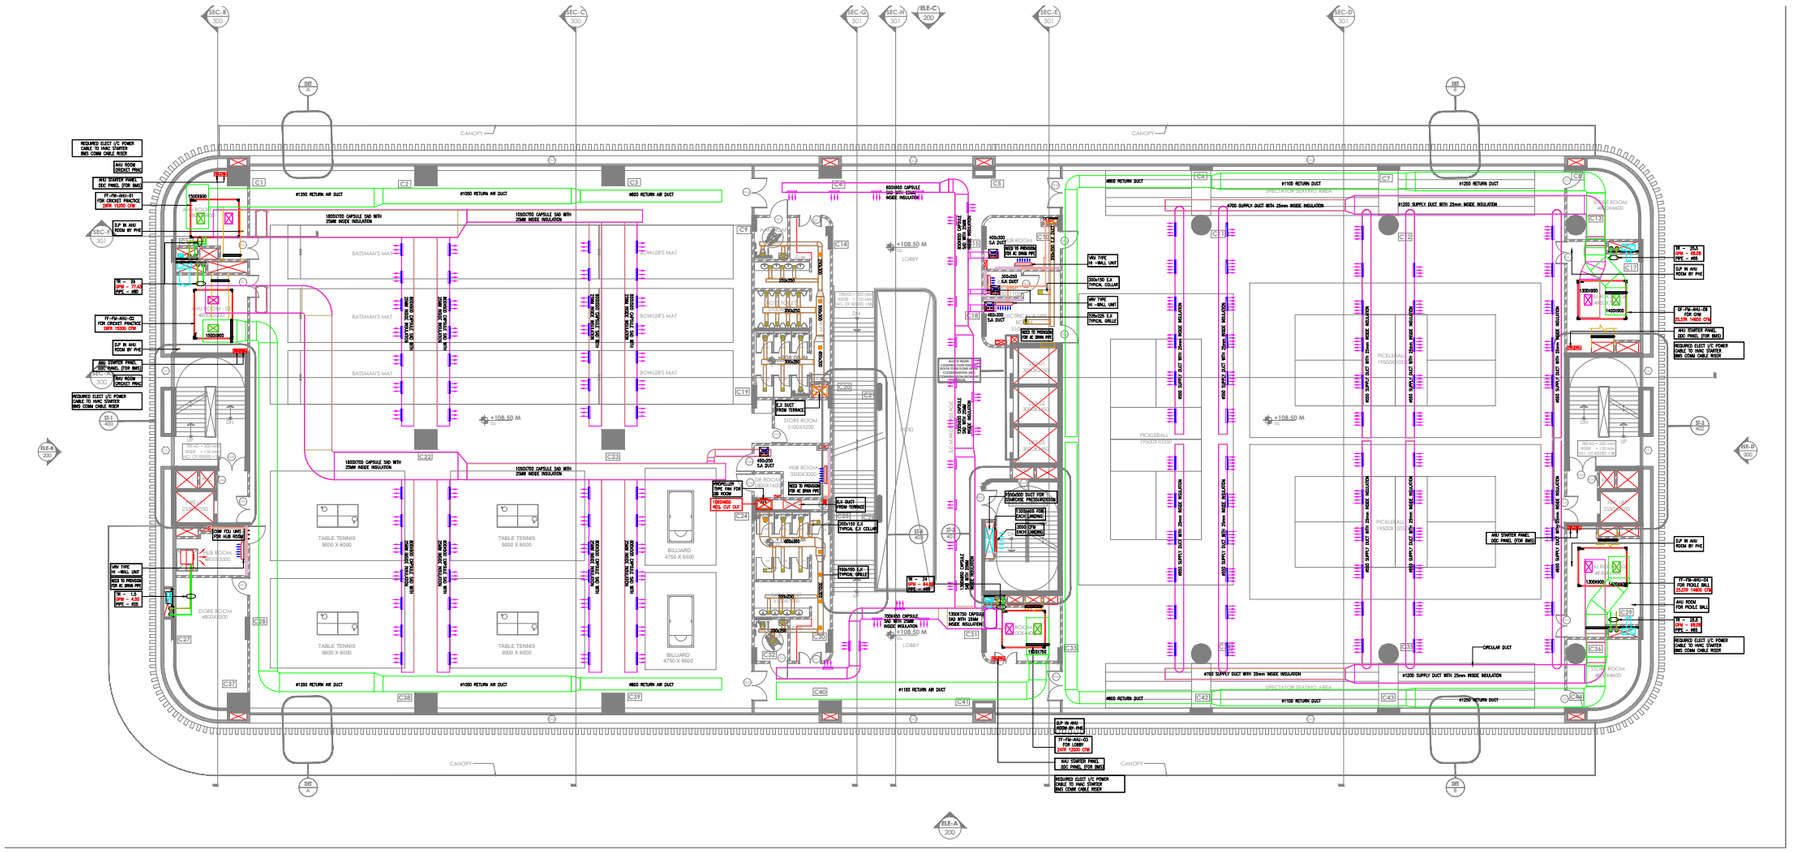


HVAC LEGEND

	AHU		RETURN AIR GRILLE		REF PIPE
	EXHAUST FAN		EXHAUST GRILLE		DRAIN PIPE
	PRESSURIZATION FAN		FA GRILLE		CHW SUPPLY PIPE
	FA. UNIT		CABINATE EXHAUST FAN		CHW RETURN PIPE
	PUMP		SUPPLY AIR DUCT		PROPELLER EX. FAN
	FCU		RETURN AIR DUCT		SIDE THROW GRILLE
			FRESH AIR DUCT		HI WALL UNIT
			TREATED FRESH AIR		VAV BOX
			EXHAUST AIR DUCT		

TENDER DRAWING

CLIENT:	MANIPAL SPORTS COMPLEX

FIRE & SECURITY CONSULTANT

KAPSE CONSULTING ENGINEERS PVT.LTD.
Unit No. 216-B, 2nd Floor, South Tower,
Lodha Supremus II, Road No. 22, Wagle Estste,
Thane West - 400604. Tel: 022 2081 0901
website : www.kapseconsultants.com

PROJECT:	JAIPUR
NAME OF STRUCTURE:	SPOTRS COMPLEX
TITLE:	PROPOSED HVAC LAYOUT_FIRST

PROJECT NO.	KCEPL/MANIPAL/JAIPUR/25-26/872	SHEET NO.	REVISION
DRAWING NO.	KCEPL/HVAC/007	2 OF 5	R1